



RUNKUTA STATION


€ STN BLDG.
RLY.Km - 1357.670
CH: 00.00M

UP ← → DN

CSTM END
BILOCHPURA STN.
AT KM: 1348.60
(DISTANCE 9.07 KM)

INTERLOCKED GATE (MANNED)
LX NO. 507 'SPL' CLASS
CH:492.00

NDLS END
KITHAM STN. AT KM: 1366.65
(DISTANCE 8.98 KM)

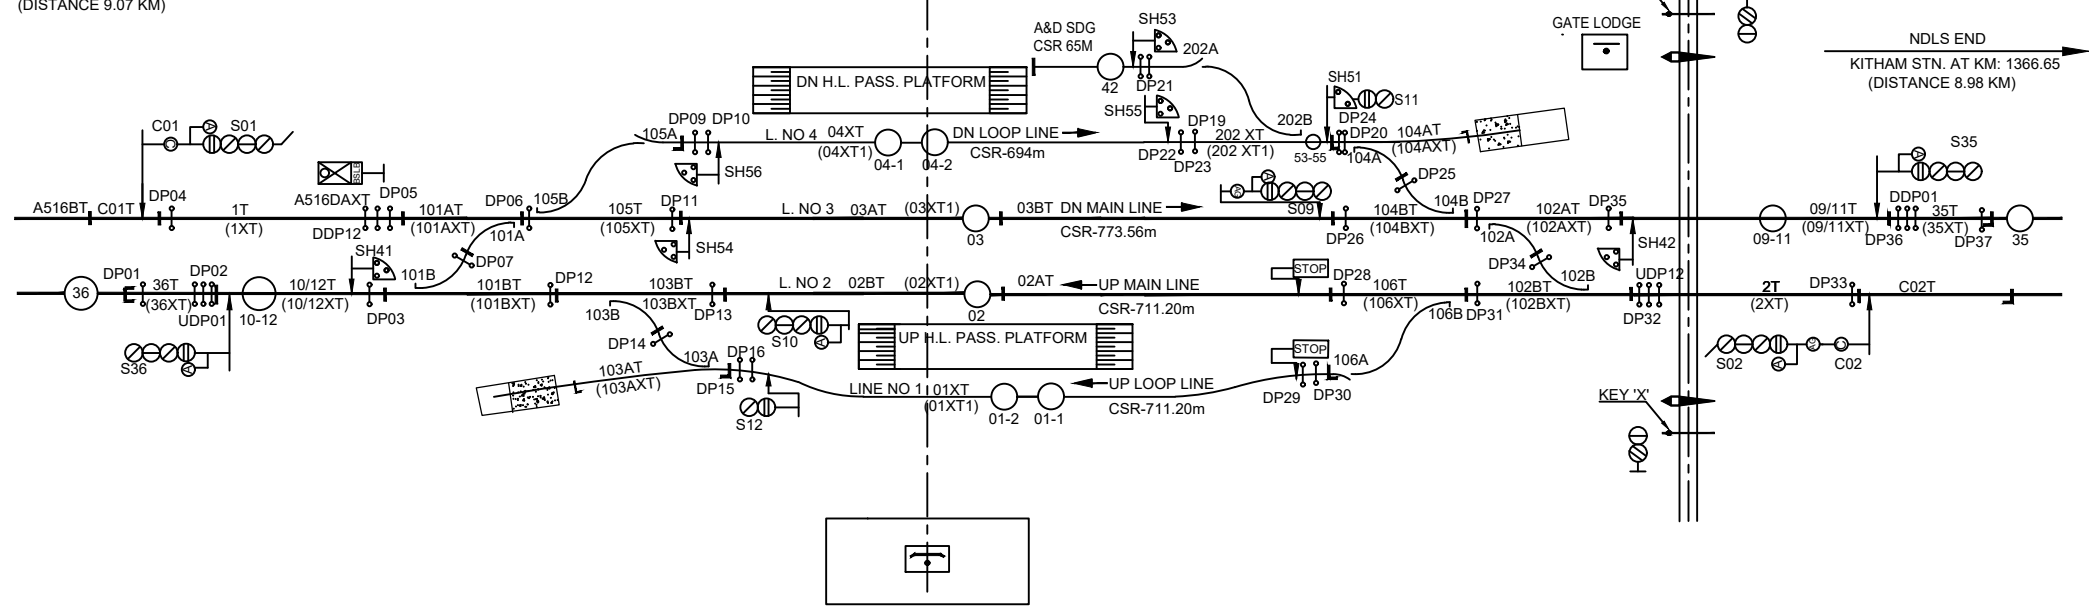

STATION BUILDING

RNKA STATION		
Sr.No.	ITEMS	Nos.
1	No. OF MAIN SIGNALS	8
2	No. OF DC TRACK CIRCUIT	22
3	No. OF POINTS (POINT MACHINES)	7 (14)
4	No. OF ROUTES	36
5	DUAL DETECTION (No. OF DP's)	37

RUNKUTA MINI